
PLANO DE PORMENOR DO POVOADO DE FACAZISSA BAIRRO FACAZISSA

Planta de Atalhoamento

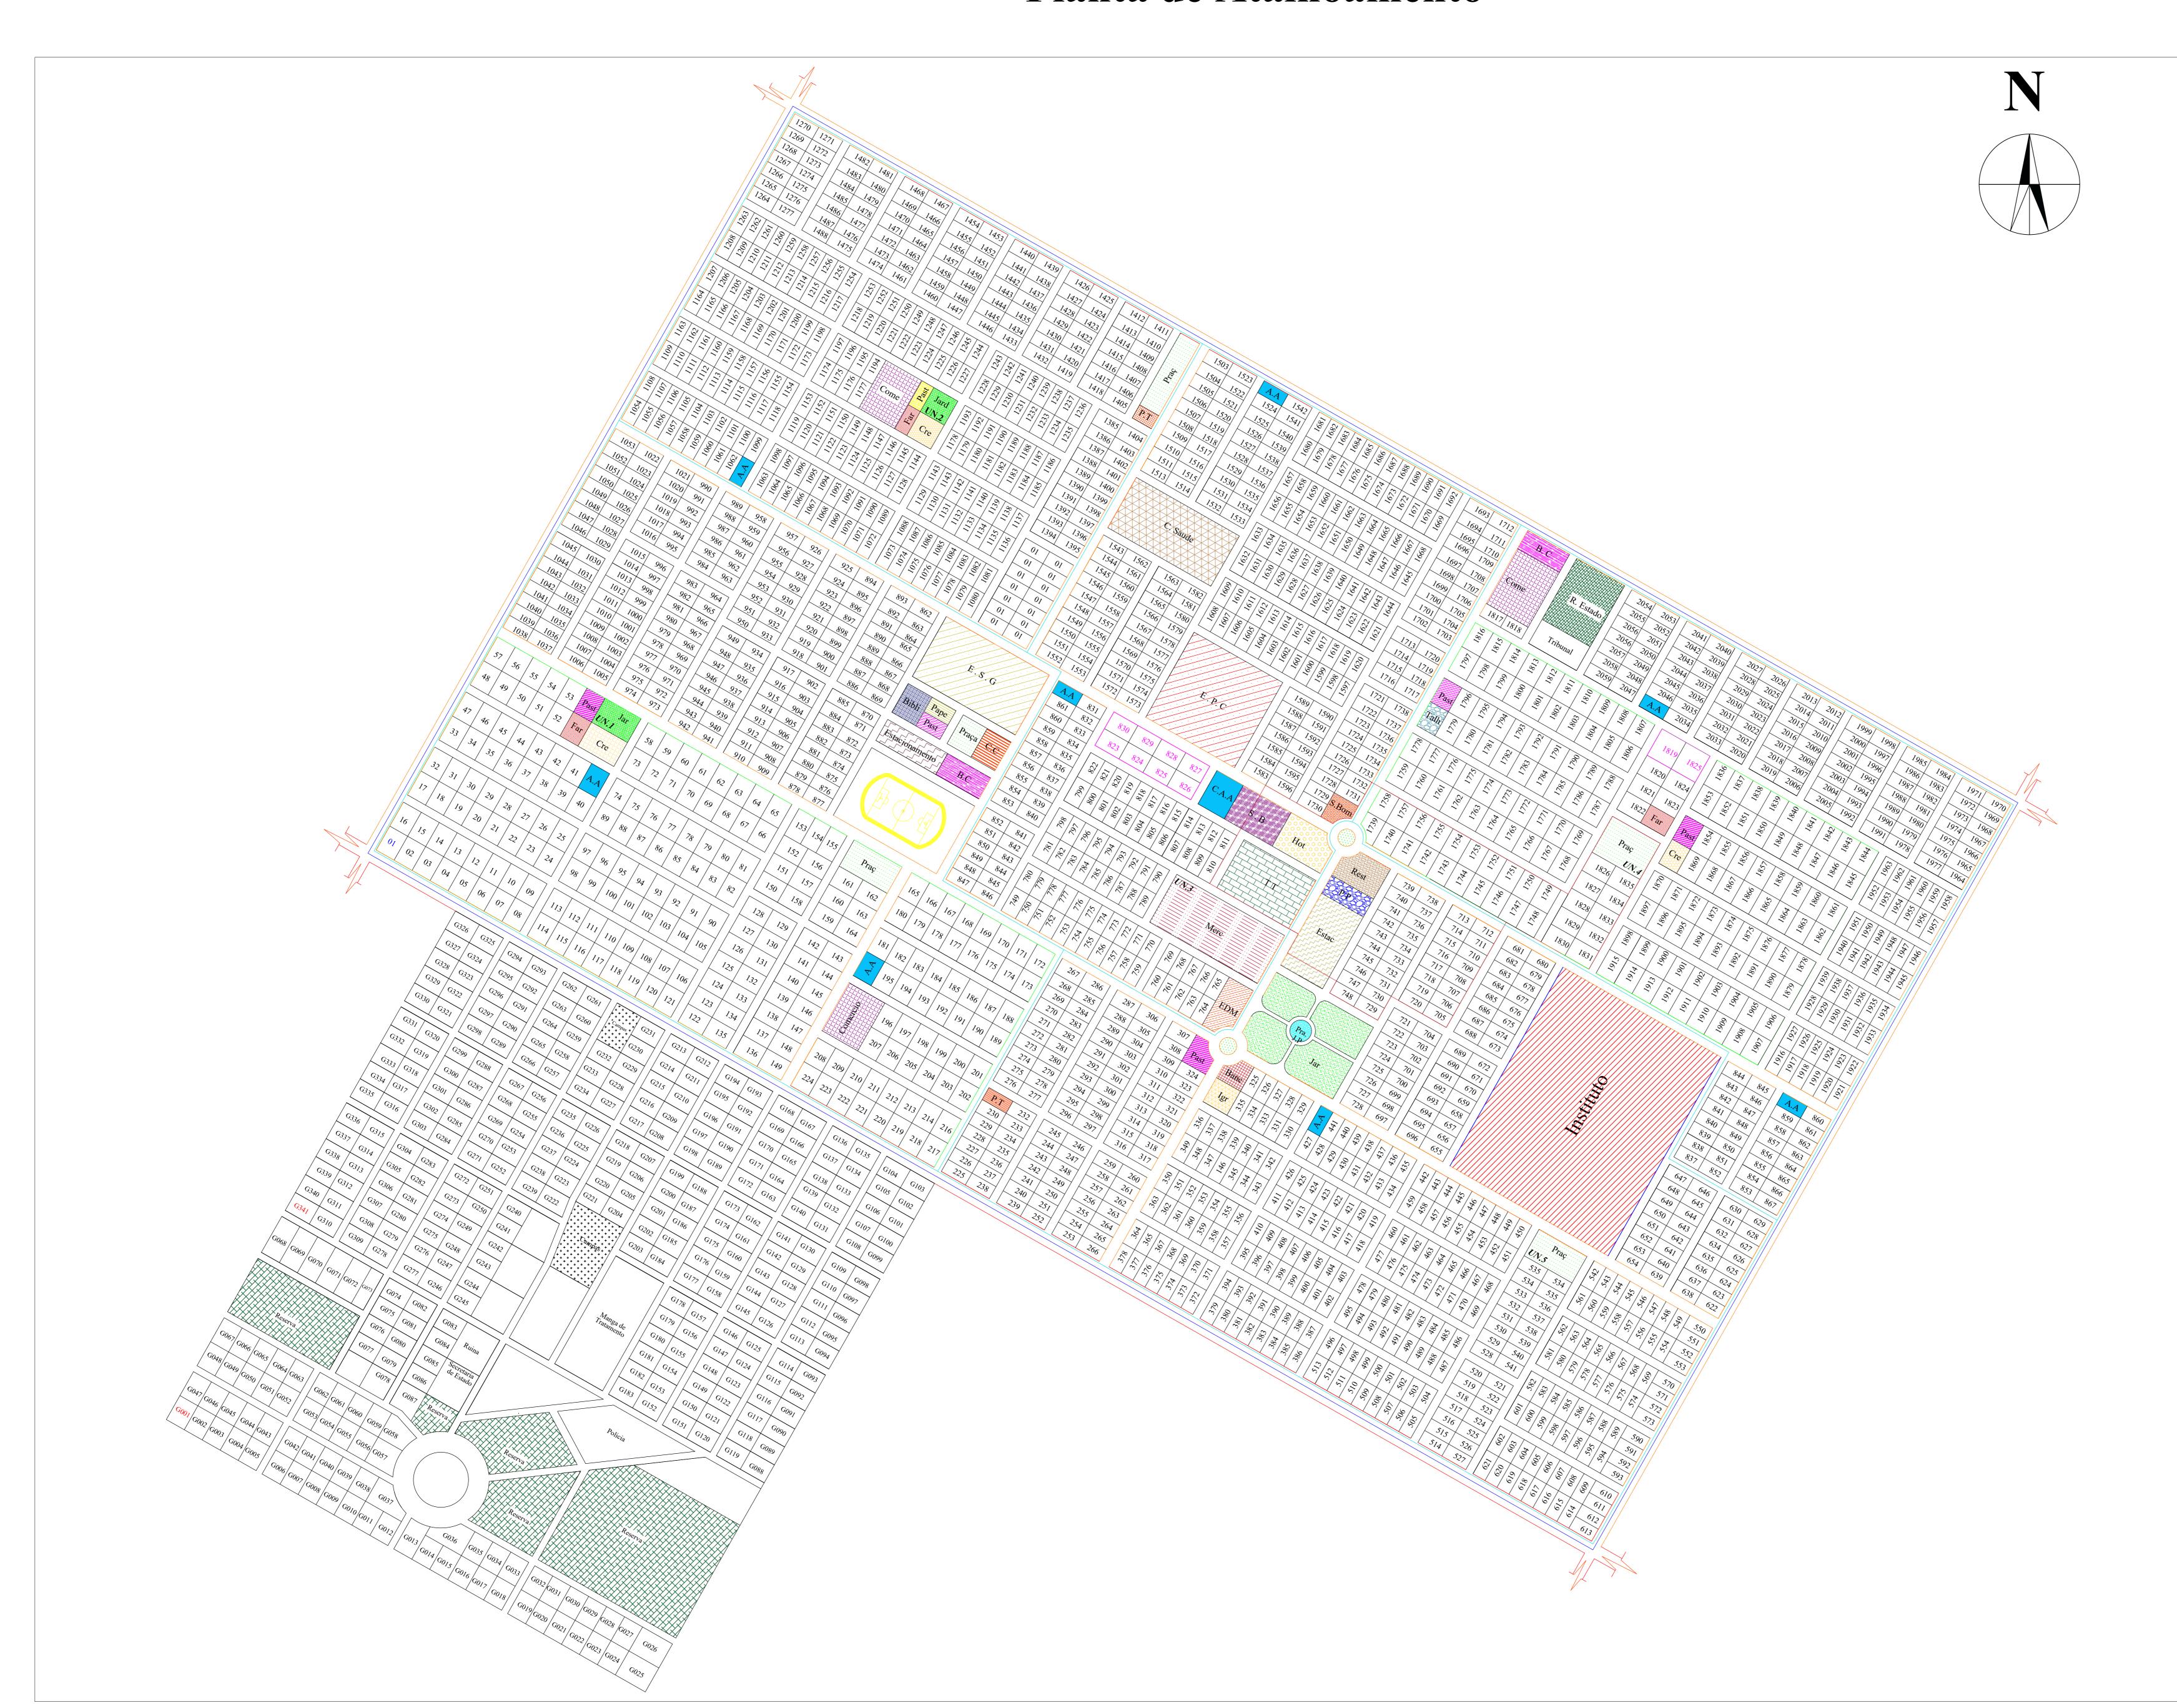



República de Moçambique Província de Maputo Governo Distrital de Magude

Legenda

Legenda					
——— Limite do Bairro					
Via Primaria					
Via Secundaria					
—— Via Terciaria					
A.A Abastecimento de Agua	Merc Mercado				
EDM Energia de Moçambique	Banc Banco				
B.C Bombas de Combustivel	Igreja				
ESG Escola Secundaria Geral	Jard Jardim				
Est Estacionamento	Praça Praça				
T.T Terminal de Transportes	Creche				
P.P. Posto Policial	Farmacia				
Rest Restaurante	Bibli Biblioteca				
S.B Sede do Bairro	PPL Papelaria				
S.Bom Serviço de Bombeiro	Hotel				
C.C Centro Cultural	Come Comercio				
Poste de Transformação	Past Pastelaria				
EPC Escola Primaria Completa	Talh Talho				
C.S Centro de Saude					

Tipoligias habitacionais

Ordem	Tipo de Construção	Área(m²)	Nº de pisos	Nº de apartamentos por edificio
1	Económica	800	1	1
2	Alto Padrão	1200	1	1
3	Alto Padrão	1120	1	1

Tipoligia dos Talhões

Tipongia dos Tamoes							
Ordem	Dimensões	Área(m²)	Nº de Talhões				
1	20x40	800	1550				
2	30x40	1200	270				
3	28x40	1120	8				
Total			1828				